

1 Feature Survey
1 : 200


Revision	Description	Date

Drawings produced in Autodesk Revit. Noted dimensions shall be taken in preference to scaling. Do not scale or dimension by hand. Verify all dimensions on site prior to construction or quote. Upon receipt of updated plans, discard previous versions.

The intellectual manifestation of this drawing and its Revit file generated origin is subject to Global copyright. Its use is subject to the approval of its owners and authors under license for implementation of a construction process specific to a single site and location. Reproduction and/or use of it, in full or part, for any other purpose without the written approval of its owners and authors is illegal and subject to prosecution.

Sheet Name		
SITE FEATURE SURVEY: ST02		
Scale: 1 : 200	at A1	Print Date 12/07/18 10:33:22 PM
Project Number 280	Project Name United - SW Hwy Byford	
Address Development Proposal 801-803 South Western Hwy, Byford, WA 6122		



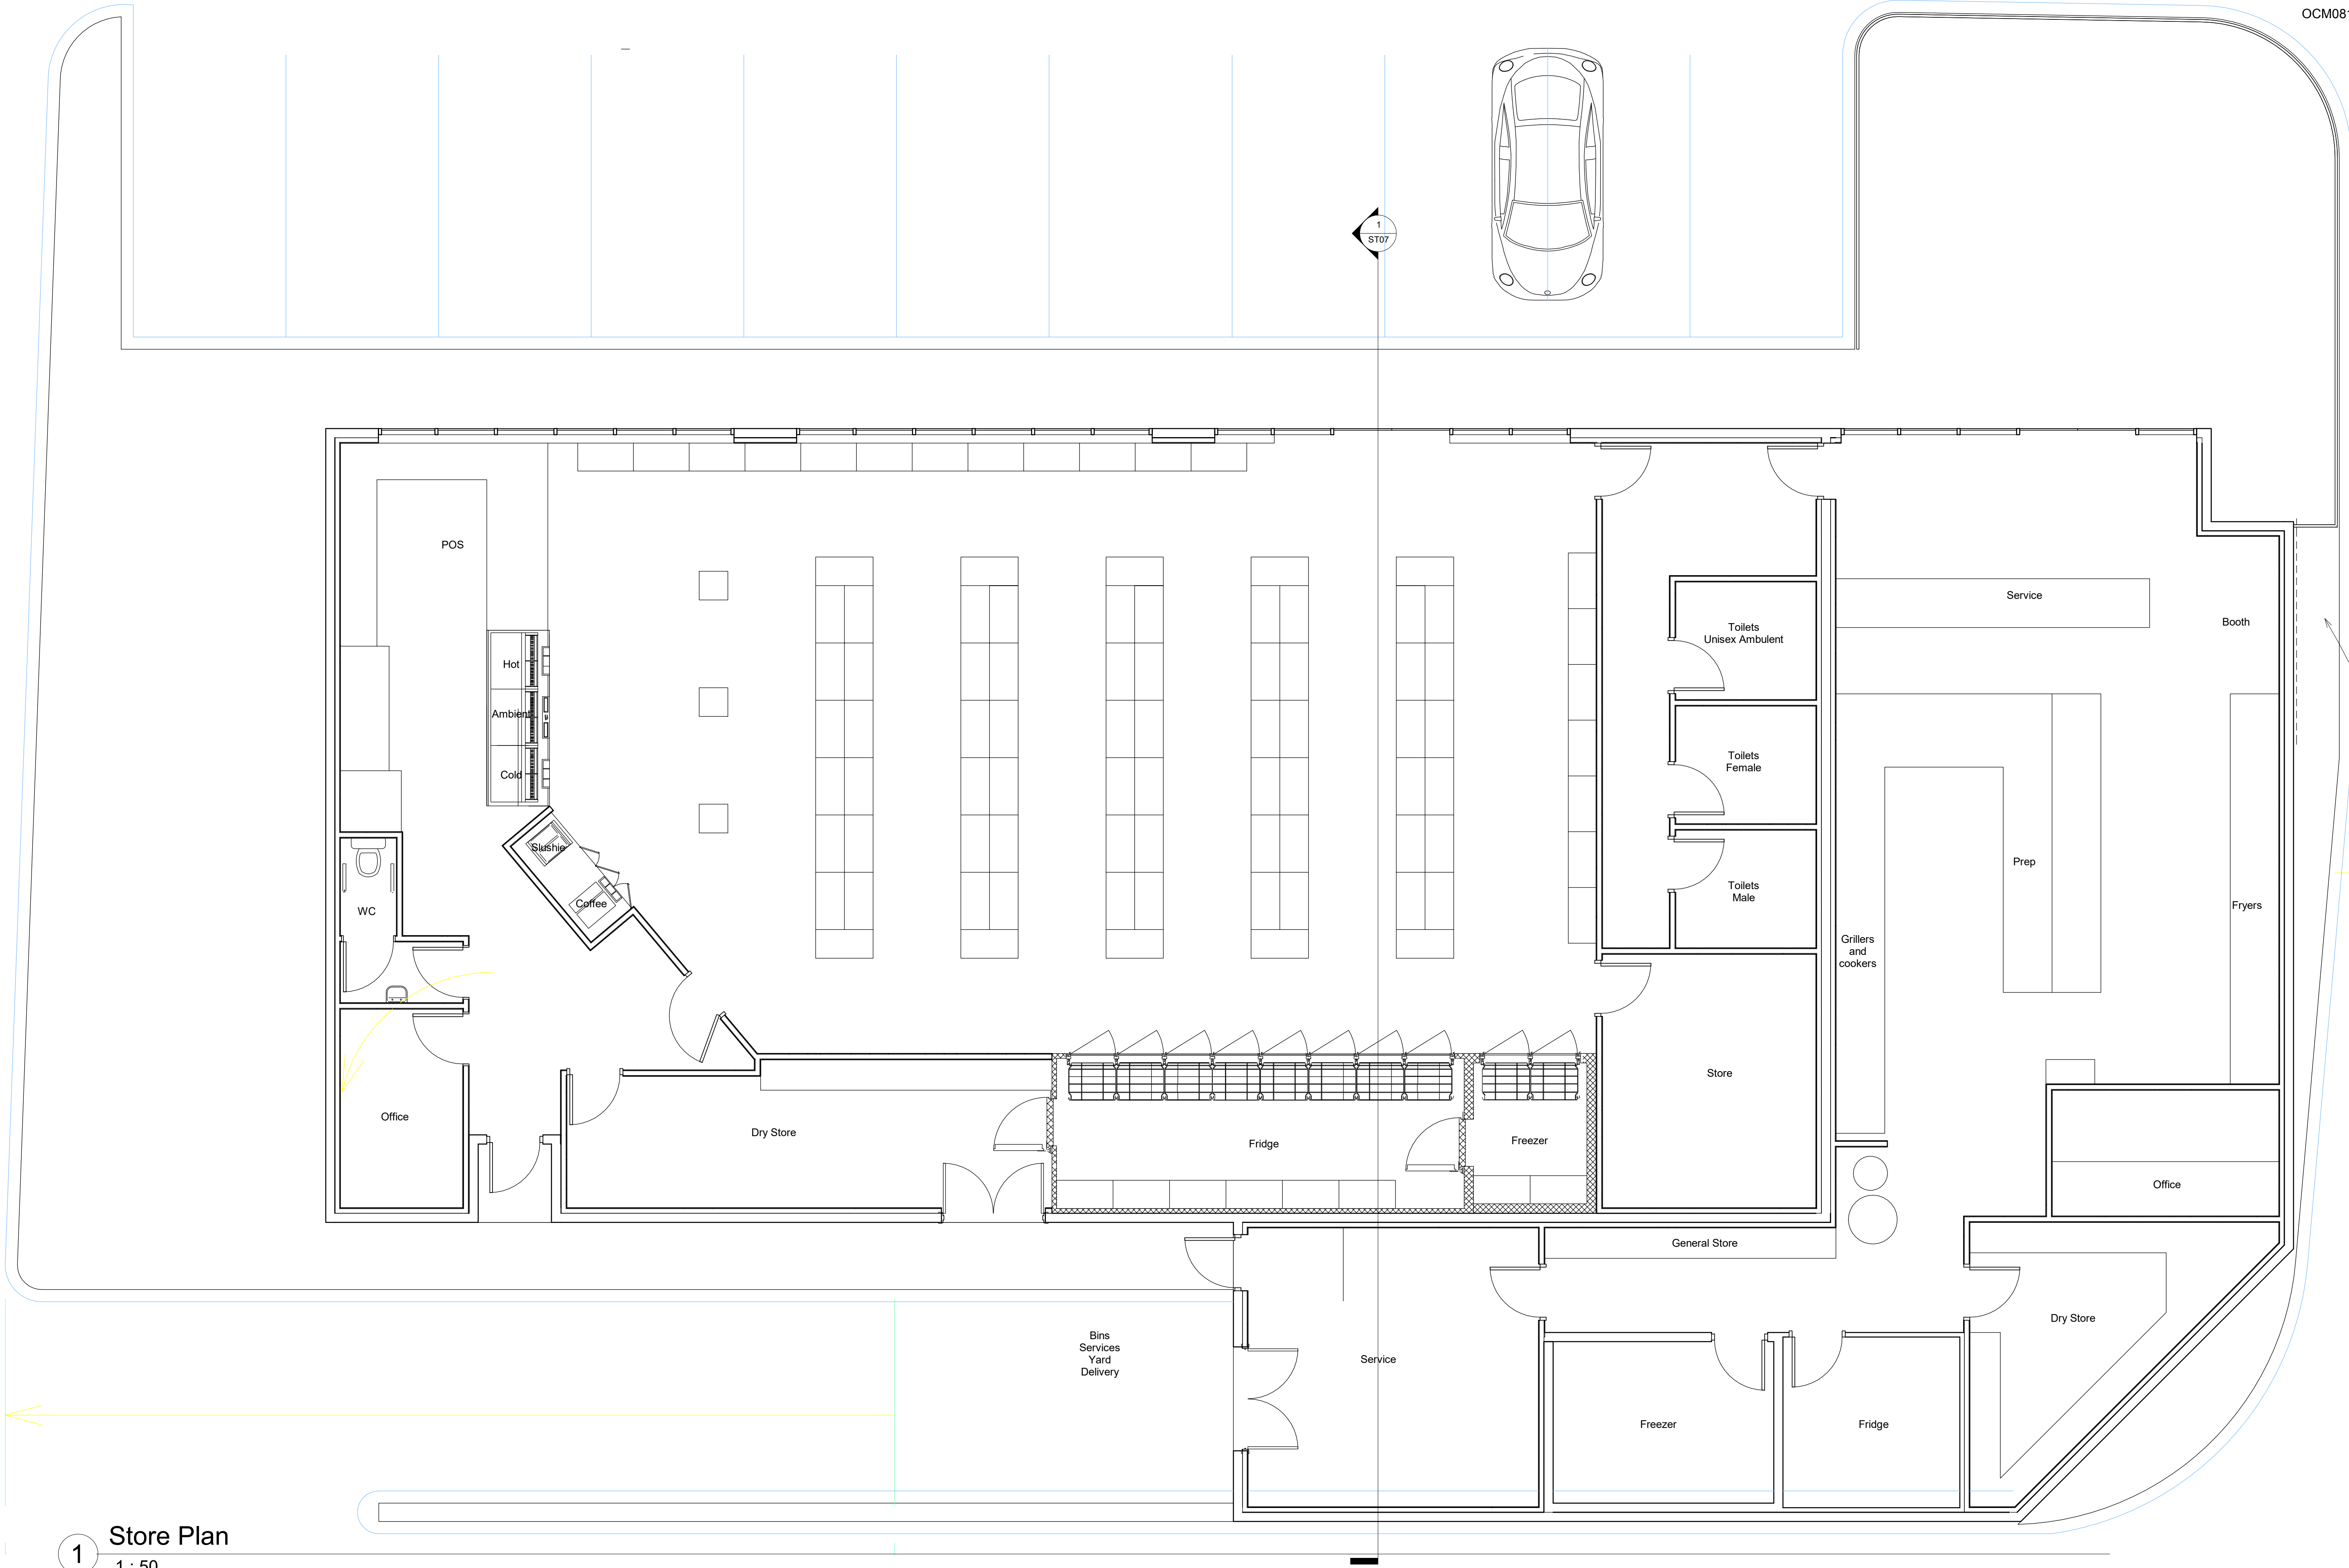


1 Store Plan
1 : 50

Revision	Description	Date


Drawings produced in Autodesk Revit. Noted dimensions shall be taken in preference to scaling. Do not scale or dimension by hand. Verify all dimensions on site prior to construction or quote. Upon receipt of updated plans, discard previous versions.

The intellectual manifestation of this drawing and its Revit file generated origin is subject to Global copyright. Its use is subject to the approval of its owners and authors under license for implementation of a construction process specific to a single site and location. Reproduction and/or use of it, in full or part, for any other purpose without the written approval of its owners and authors is illegal and subject to prosecution.

Sheet Name		
STORE PLAN: ST04		
Scale: 1 : 50	at A1	Print Date 12/07/18 10:33:29 PM
Project Number 280	Project Name United - SW Hwy Byford	
Address Development Proposal 801-803 South Western Hwy, Byford, WA 6122		



UNITED PETROLEUM PTY LTD
200 HOODLE STREET ABBOTSFORD, VICTORIA 3067
TELEPHONE 03 9413 1400 FACSIMILE 03 9413 1401



HANDCRAFTED OVEN FRESH



aspire | commit | create

70 Belmont Ave Belmont WA Australia 6104 | +61 8 9416 0666

PRELIMINARY






LAWRENCE ASSOCIATES
ARCHITECTURE . DESIGN . PROJECT MANAGEMENT

www.lapl.com.au 0404 864 146 contact@lapl.com.au

Ordinary Council Meeting 27 August 2018

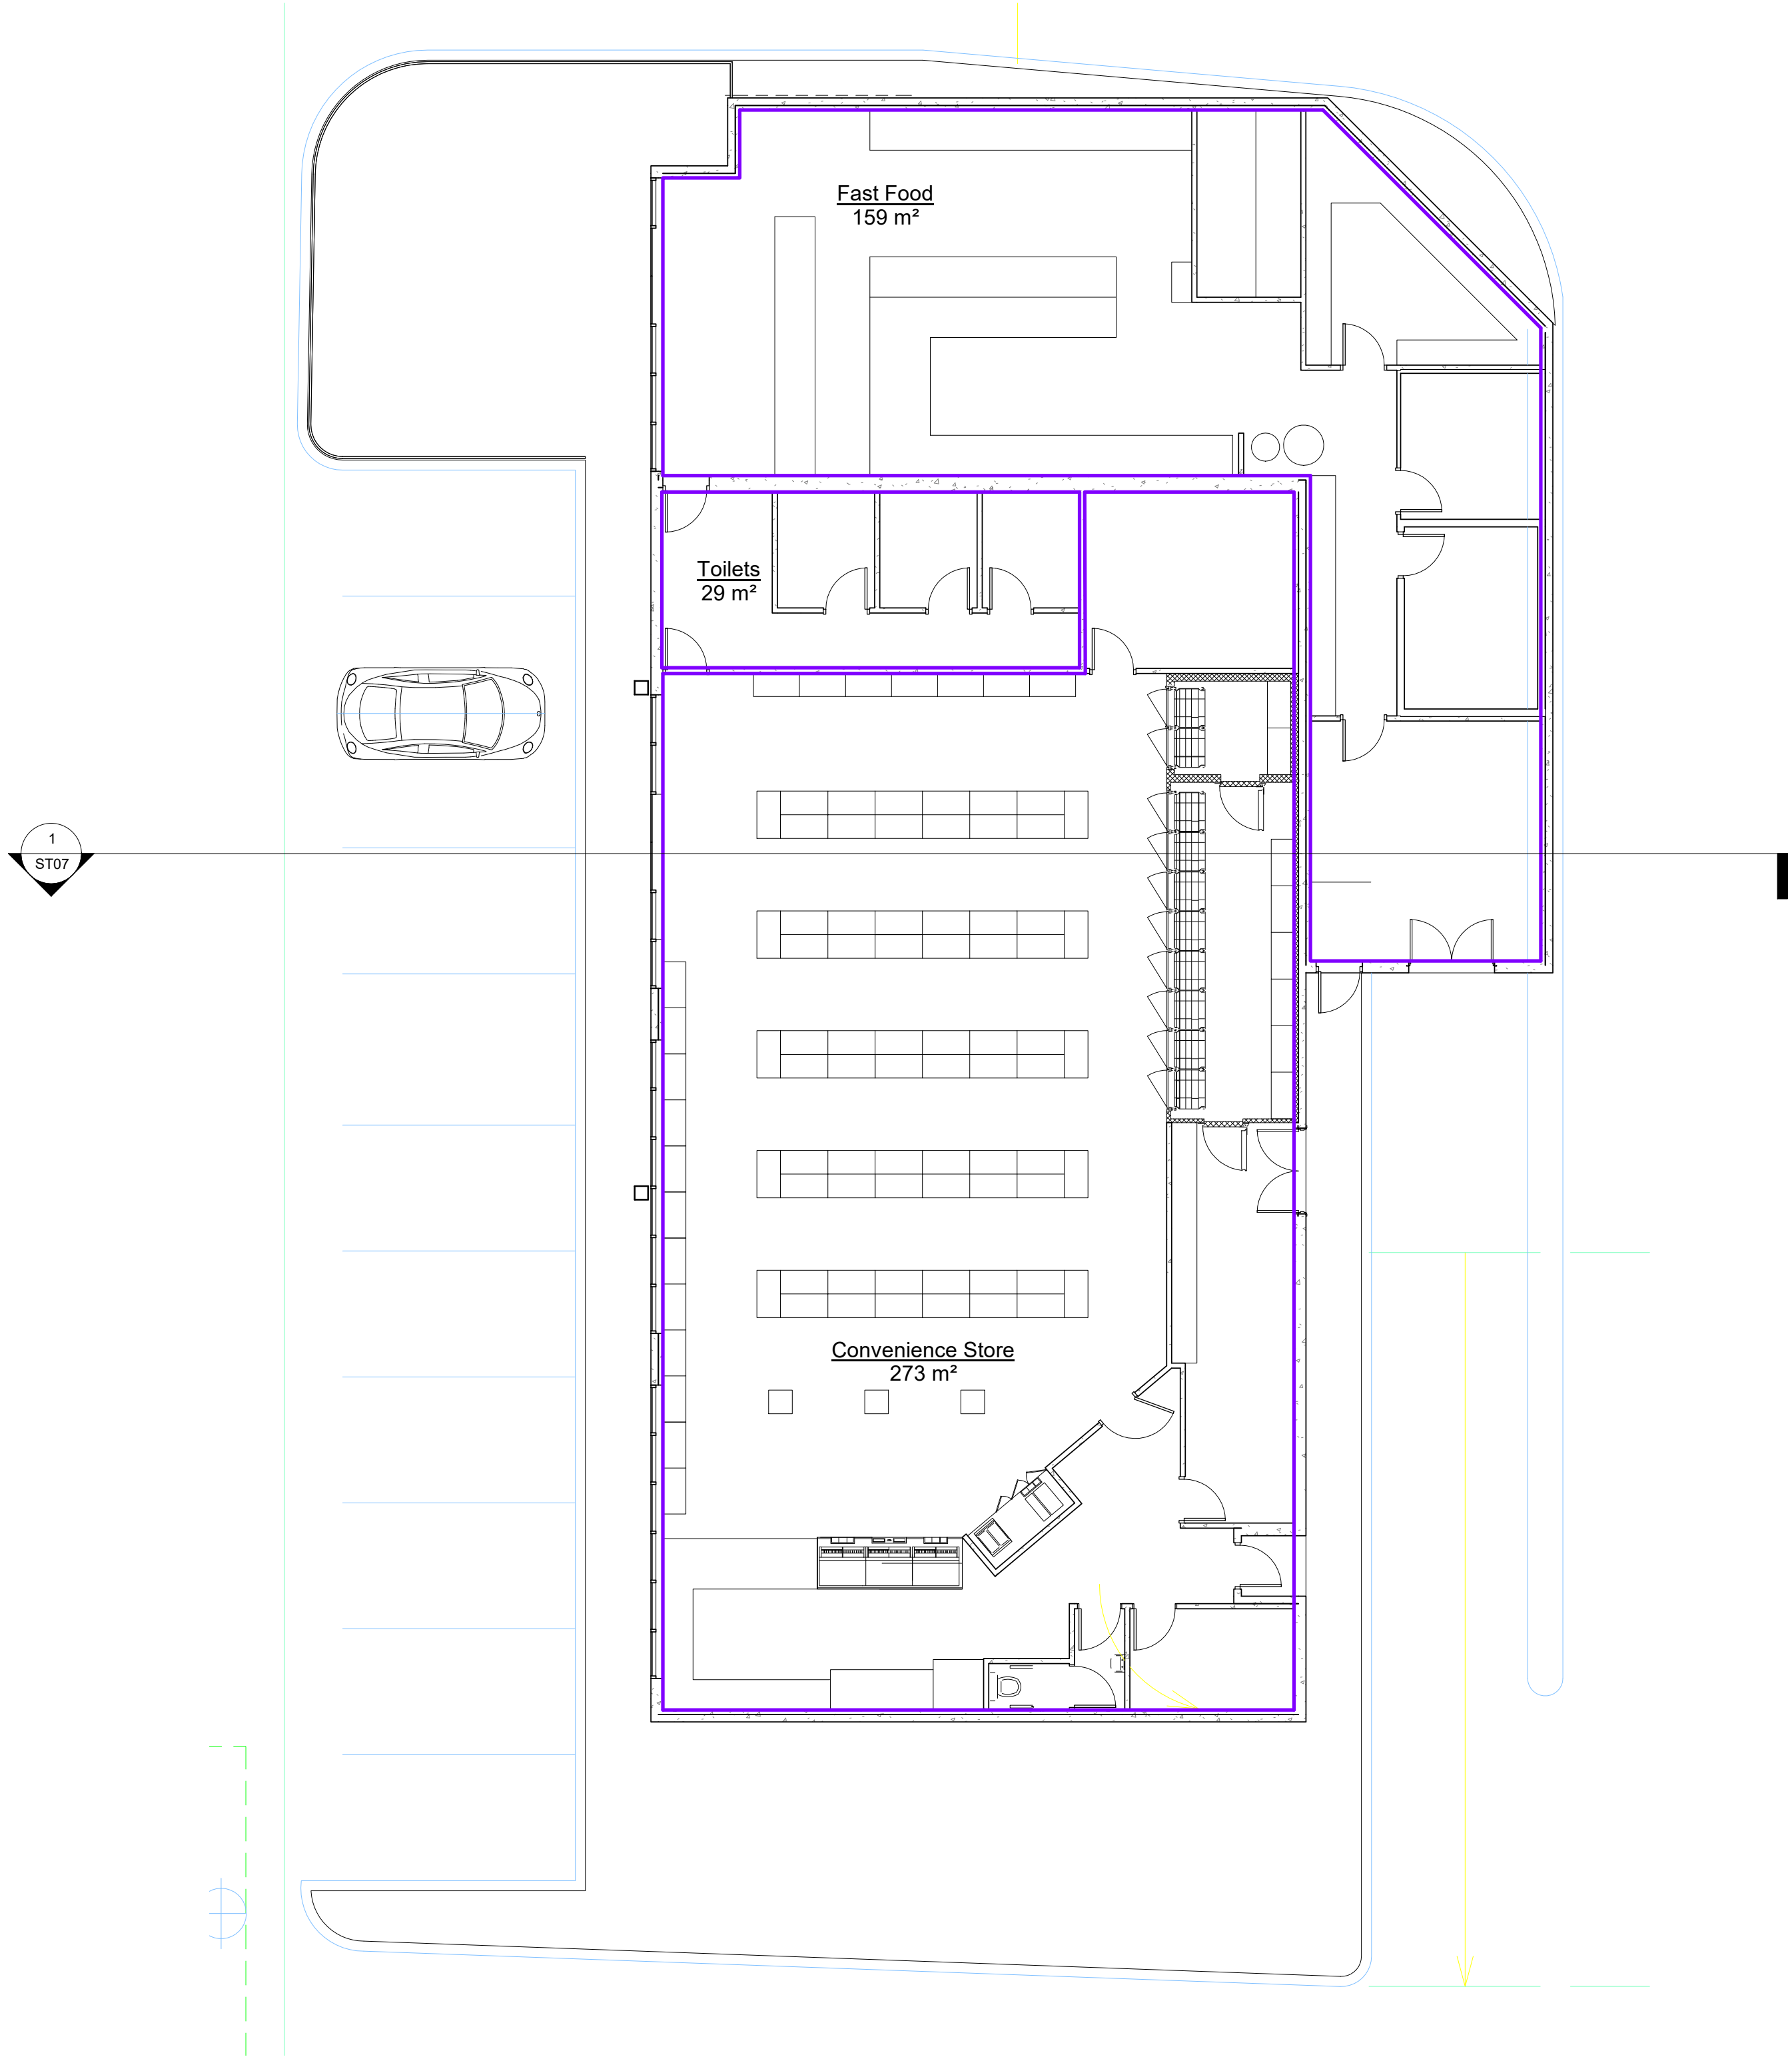

1 Building FL
1 : 100

Revision	Description	Date

Drawings produced in Autodesk Revit. Noted dimensions shall be taken in preference to scaling. Do not scale or dimension by hand. Verify all dimensions on site prior to construction or quote. Upon receipt of updated plans, discard previous versions.

The intellectual manifestation of this drawing and its Revit file generated origin is subject to Global copyright. Its use is subject to the approval of its owners and authors under license for implementation of a construction process specific to a single site and location. Reproduction and/or use of it, in full or part, for any other purpose without the written approval of its owners and authors is illegal and subject to prosecution.

Sheet Name		
AREA PLAN: ST29		
Scale: 1 : 100	at A1	Print Date 12/07/18 10:34:34 PM
Project Number 280	Project Name United - SW Hwy Byford	
Address Development Proposal 801-803 South Western Hwy, Byford, WA 6122		

